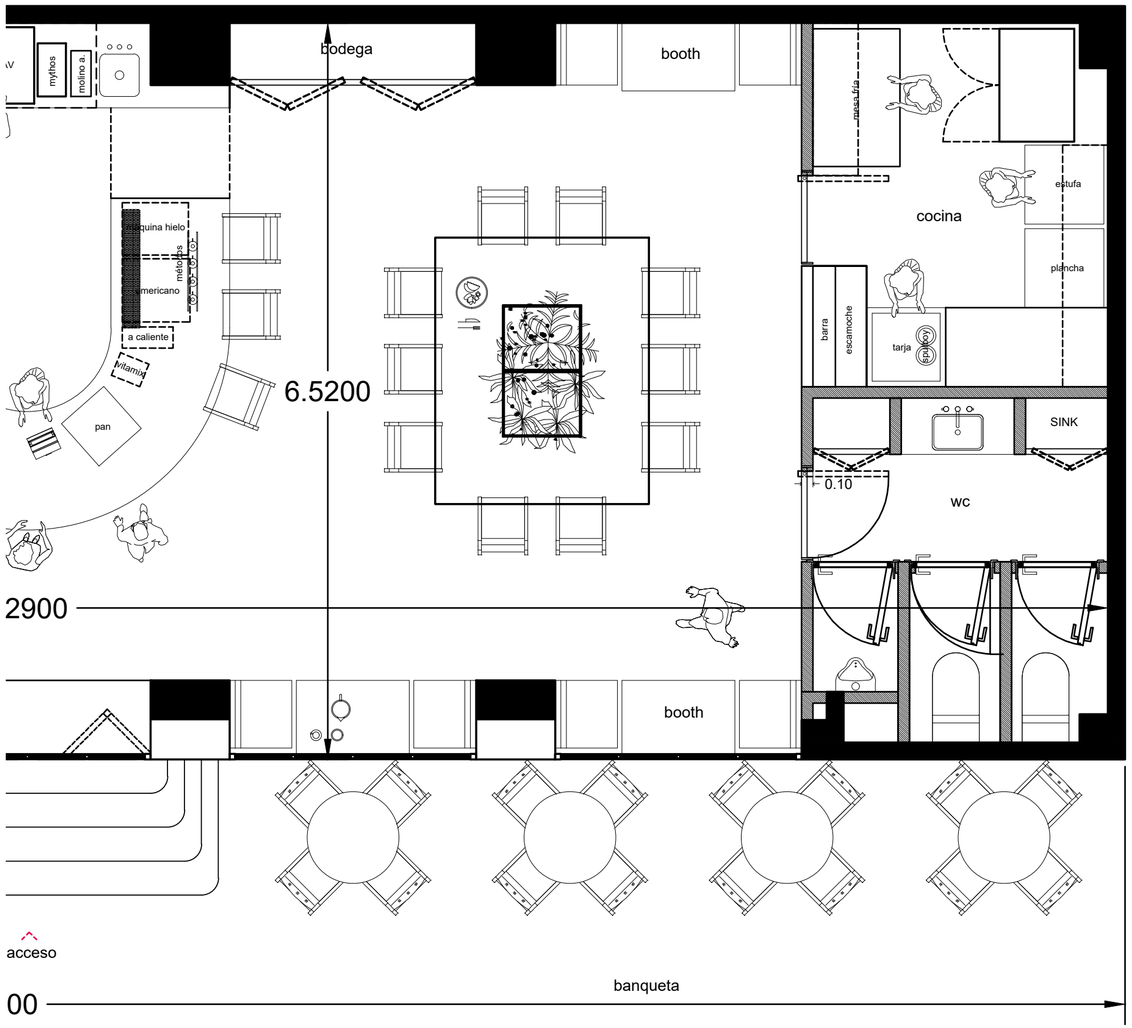

A course by Mònica Vega

PLANS FOR YOUR PROJECT

You can download the plans for the final project here.

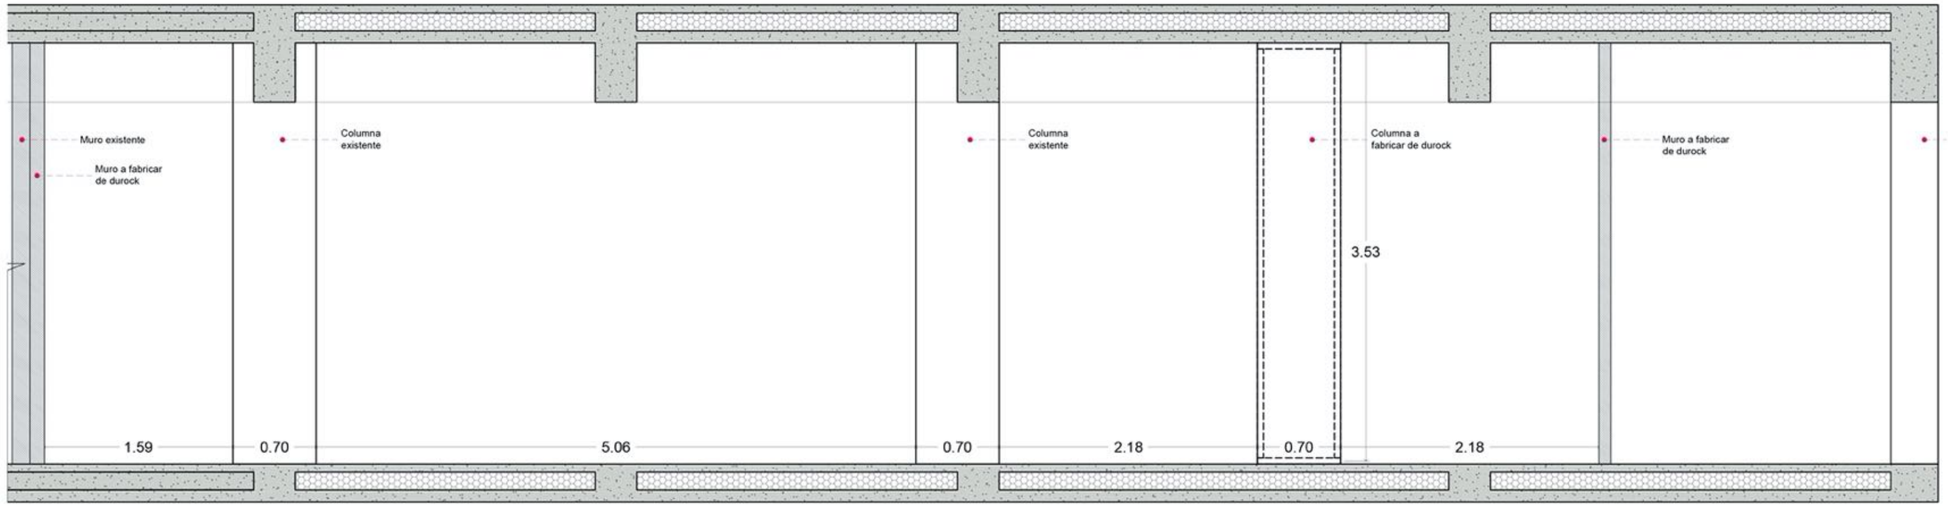

SECTION B-B ESC 1:30

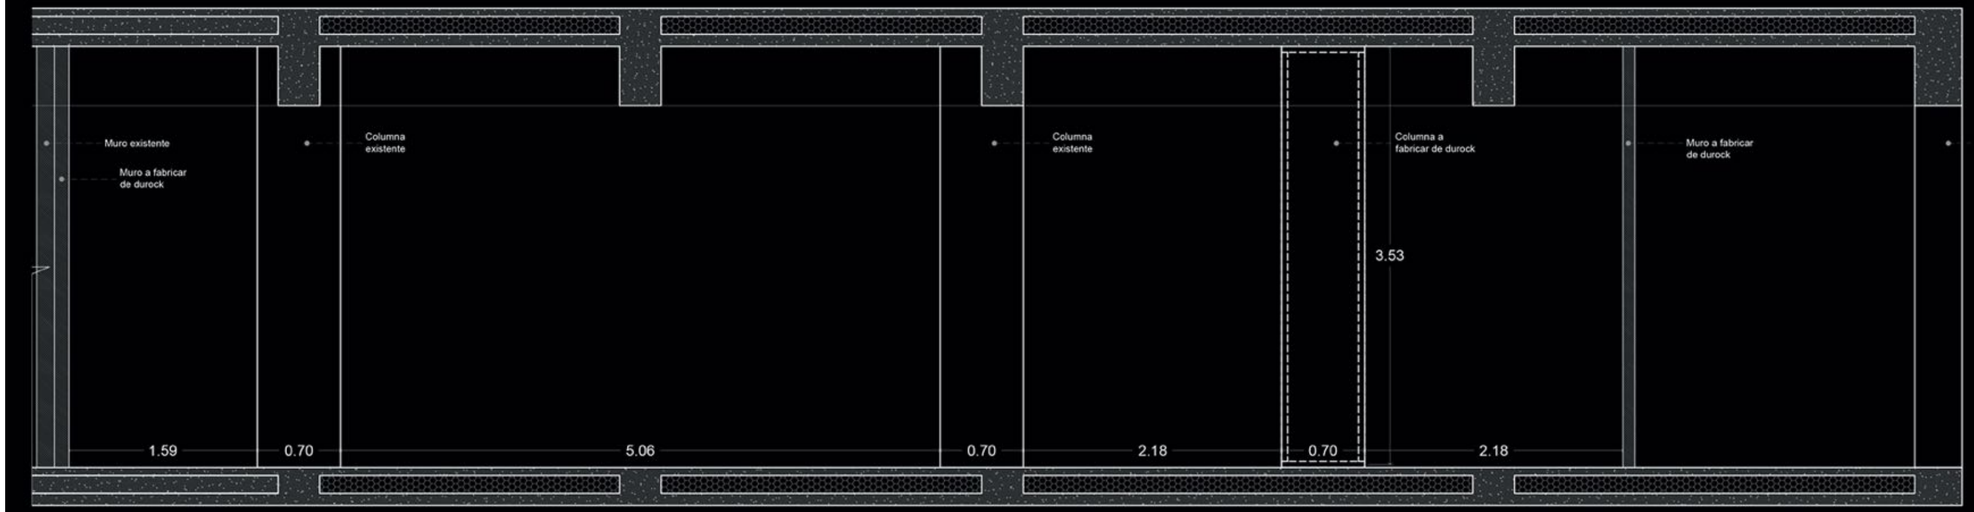

SECTION B-B ESC 1:30

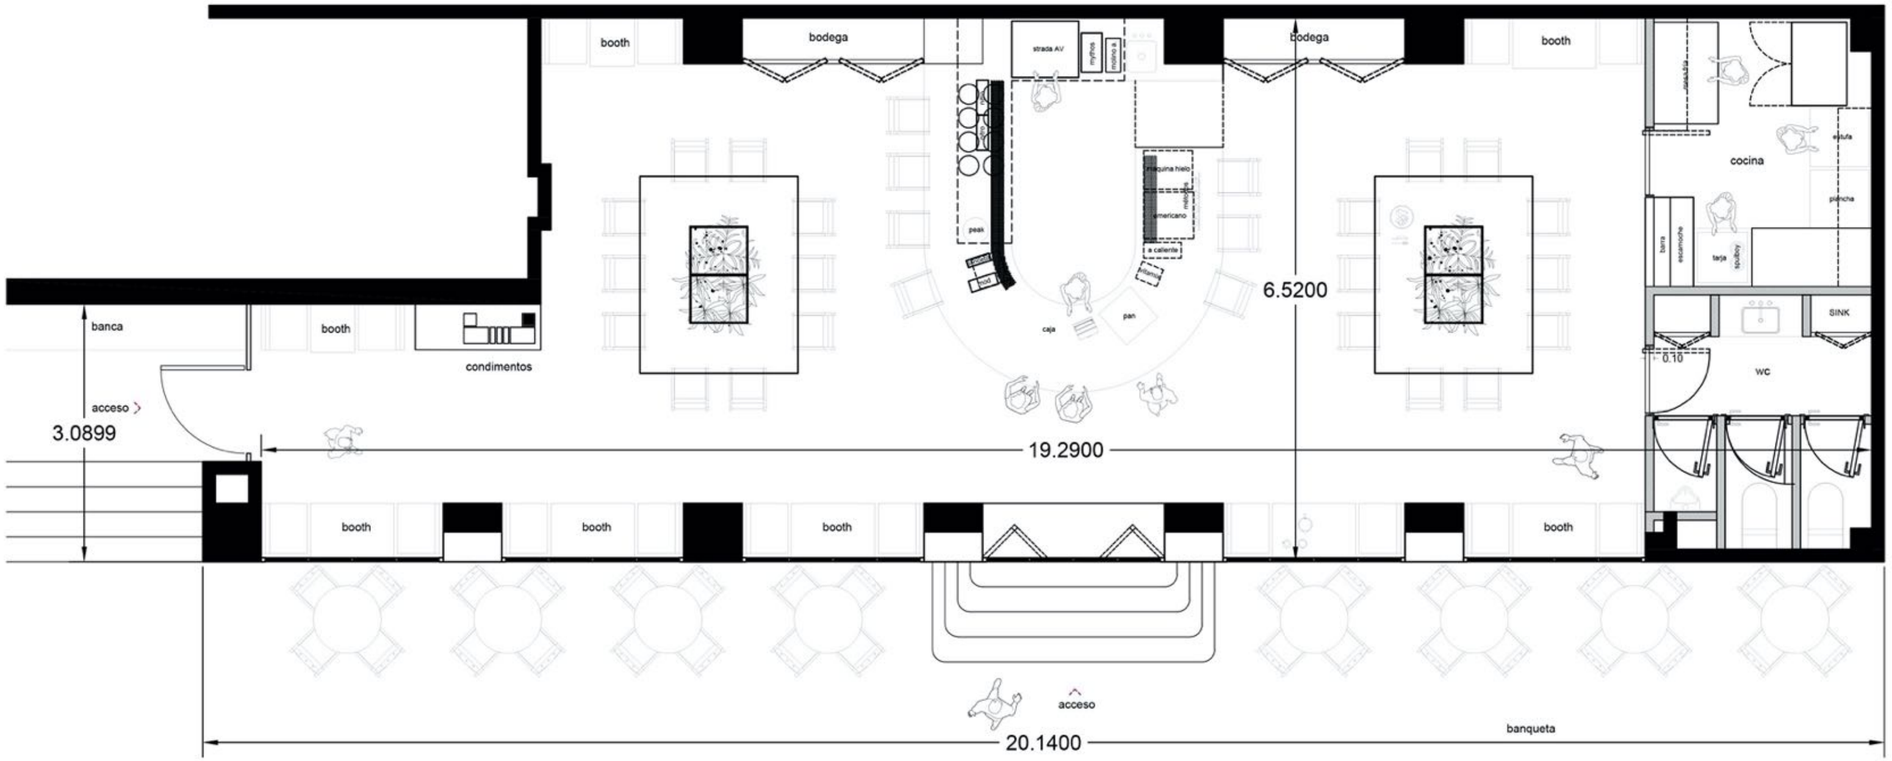
booth
bodega
strada AV
mythos
pedido
bodega
booth
cocina
estufa
plancha
barra
escarcha
tarja
spoiby
SINK
0.10
wc
máquina hielo
americano
a caliente
pan
caja
pean
6.5200
banca
booth
condimentos
acceso
3.0899
19.2900
booth
booth
booth
booth
acceso
20.1400
banqueta

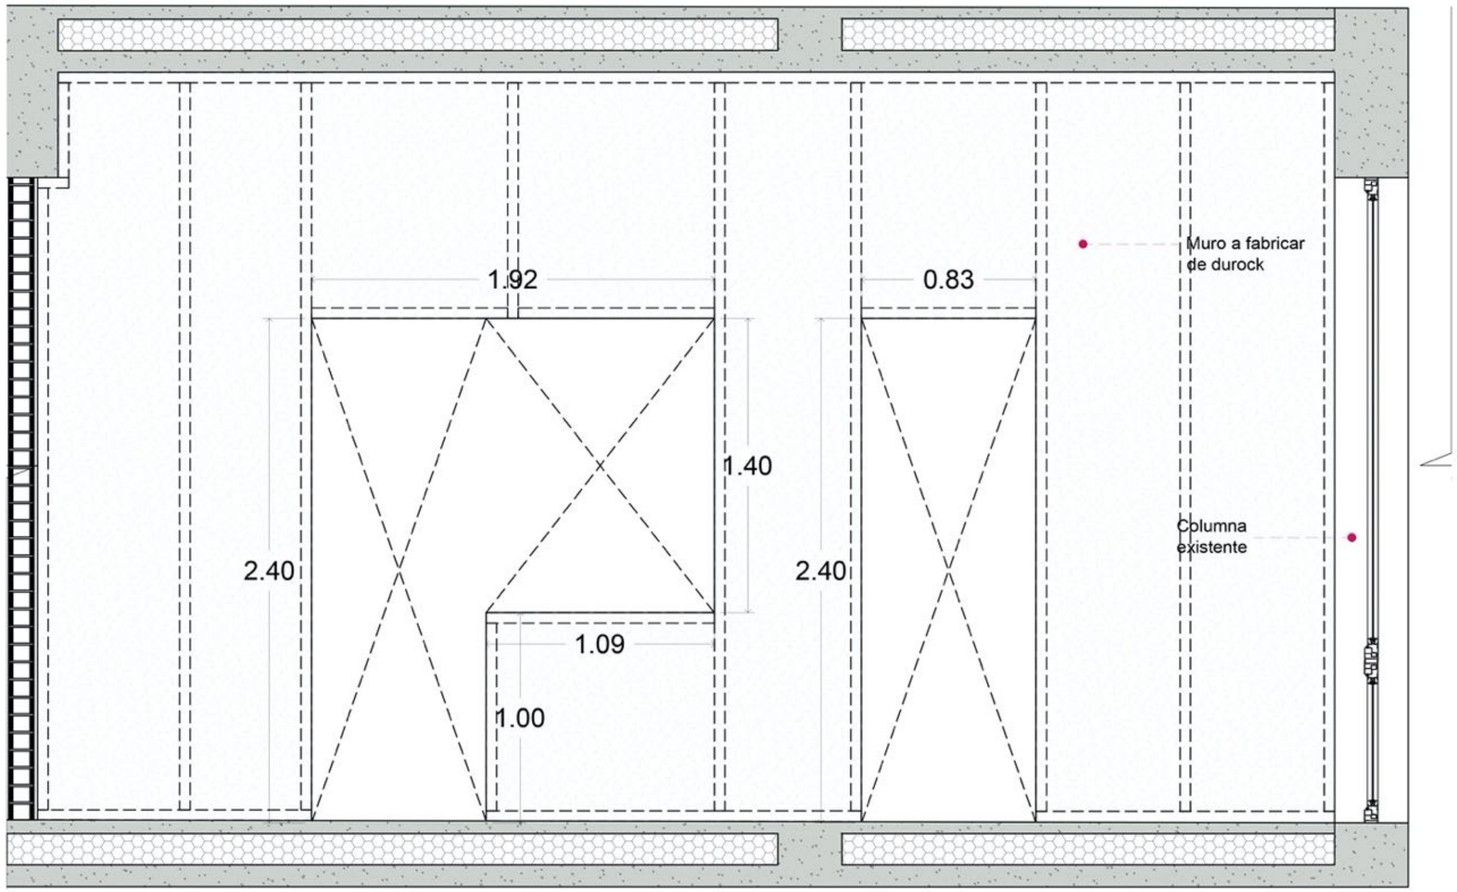

SECTION A-A ESC 1:30

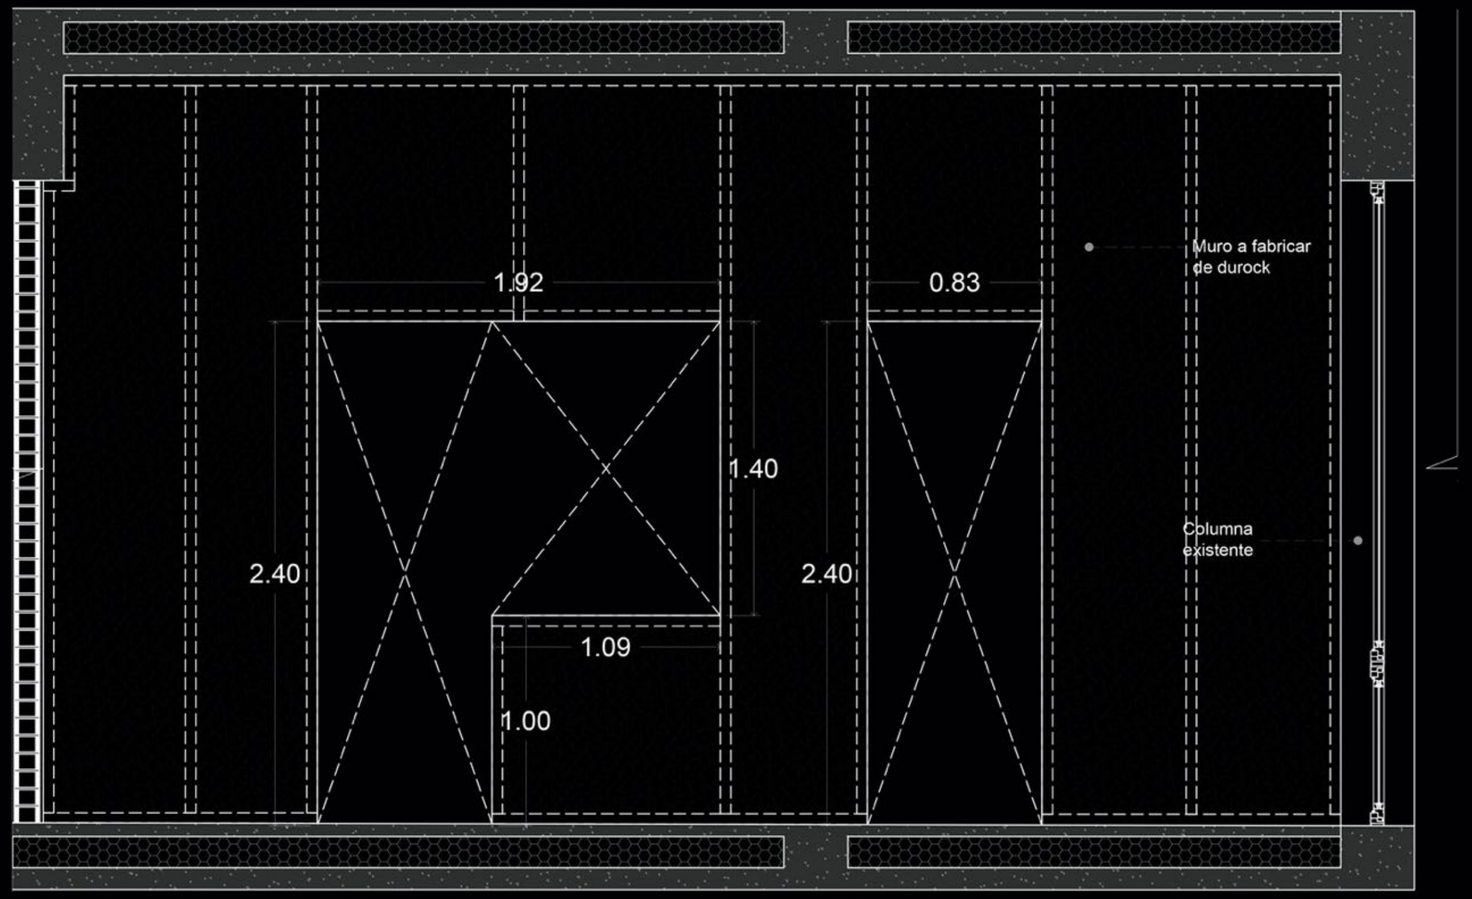

SECTION B-B ESC 1:30

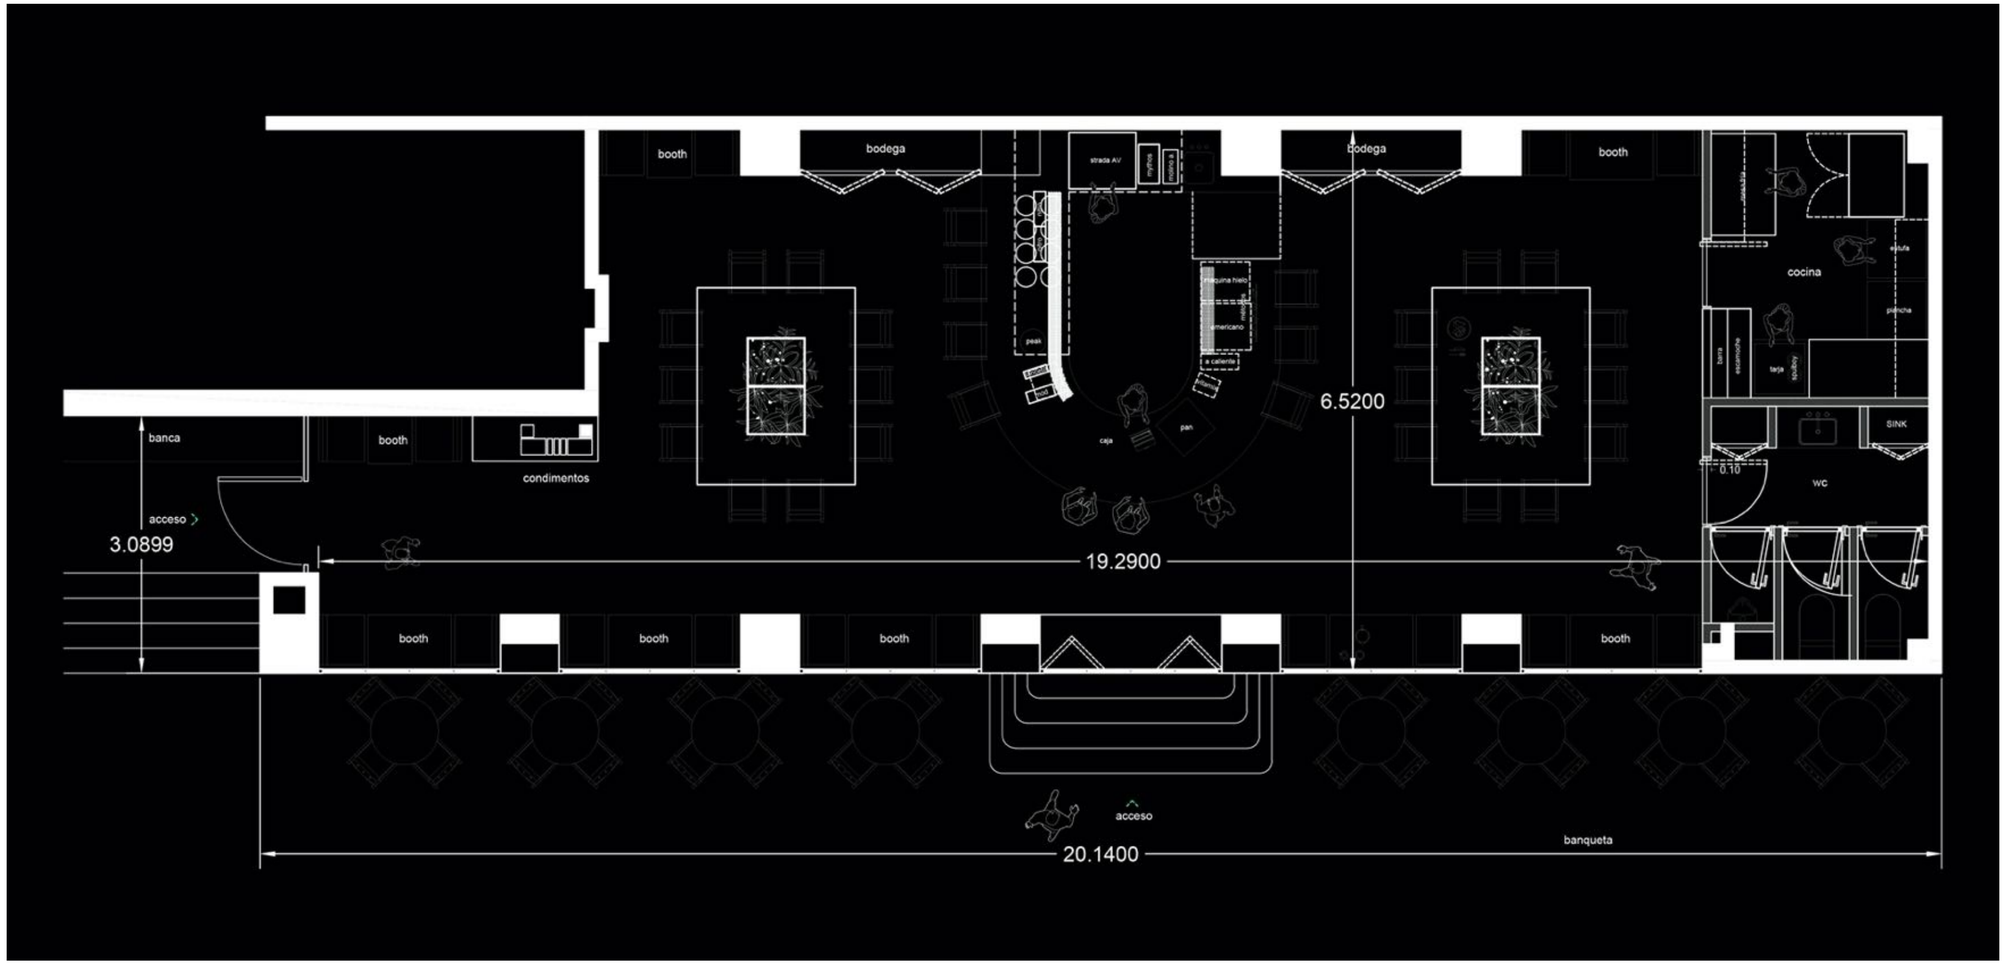
booth
bodega
bodega
booth
cocina
estufa
plancha
barra
escamoche
tarja
spoilby
SINK
wc
0.10
banca
booth
condimentos
acceso
3.0899
6.5200
19.2900
caja
pan
booth
booth
booth
booth
acceso
20.1400
banqueta

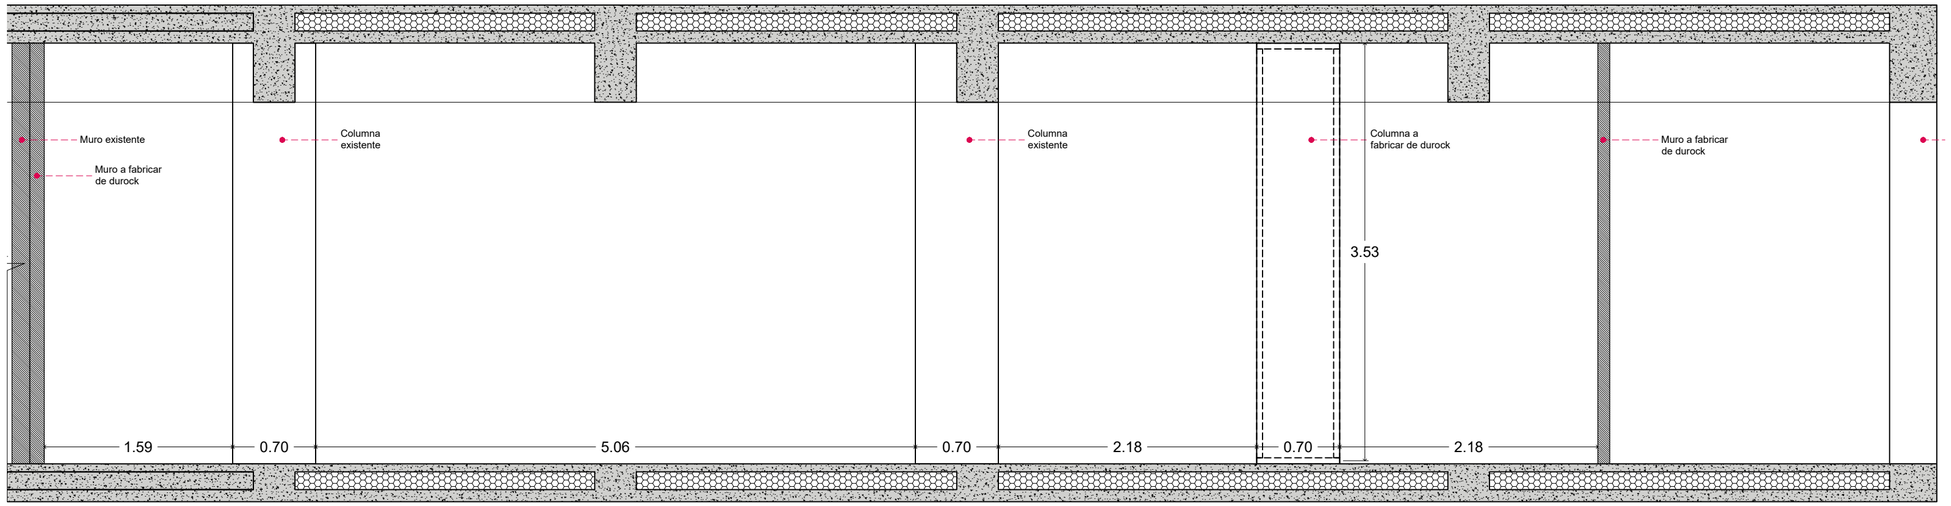

SECTION B-B ESC 1:30

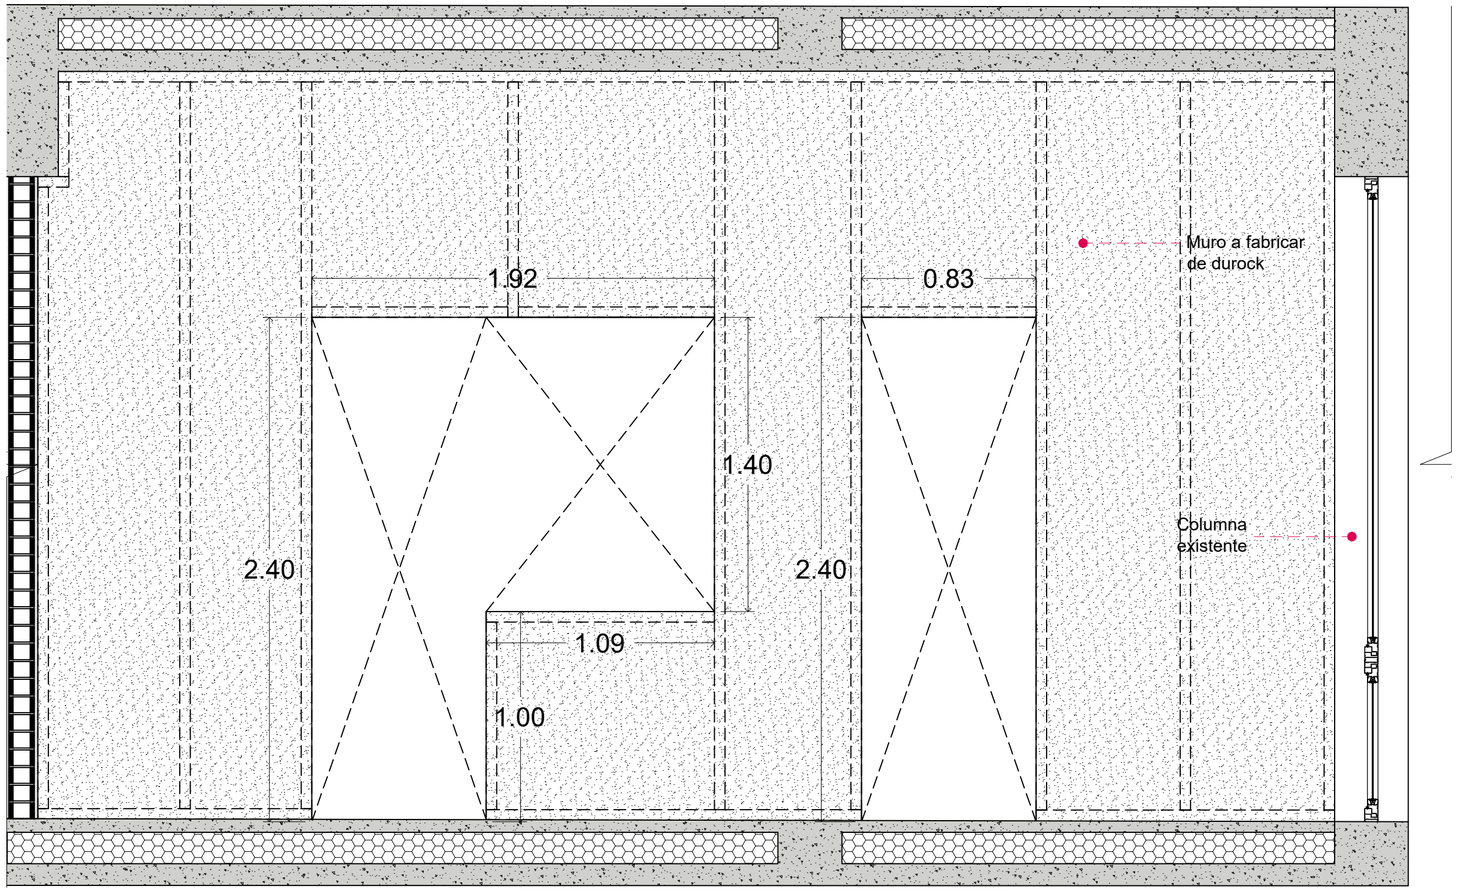

SECTION A-A ESC 1:30

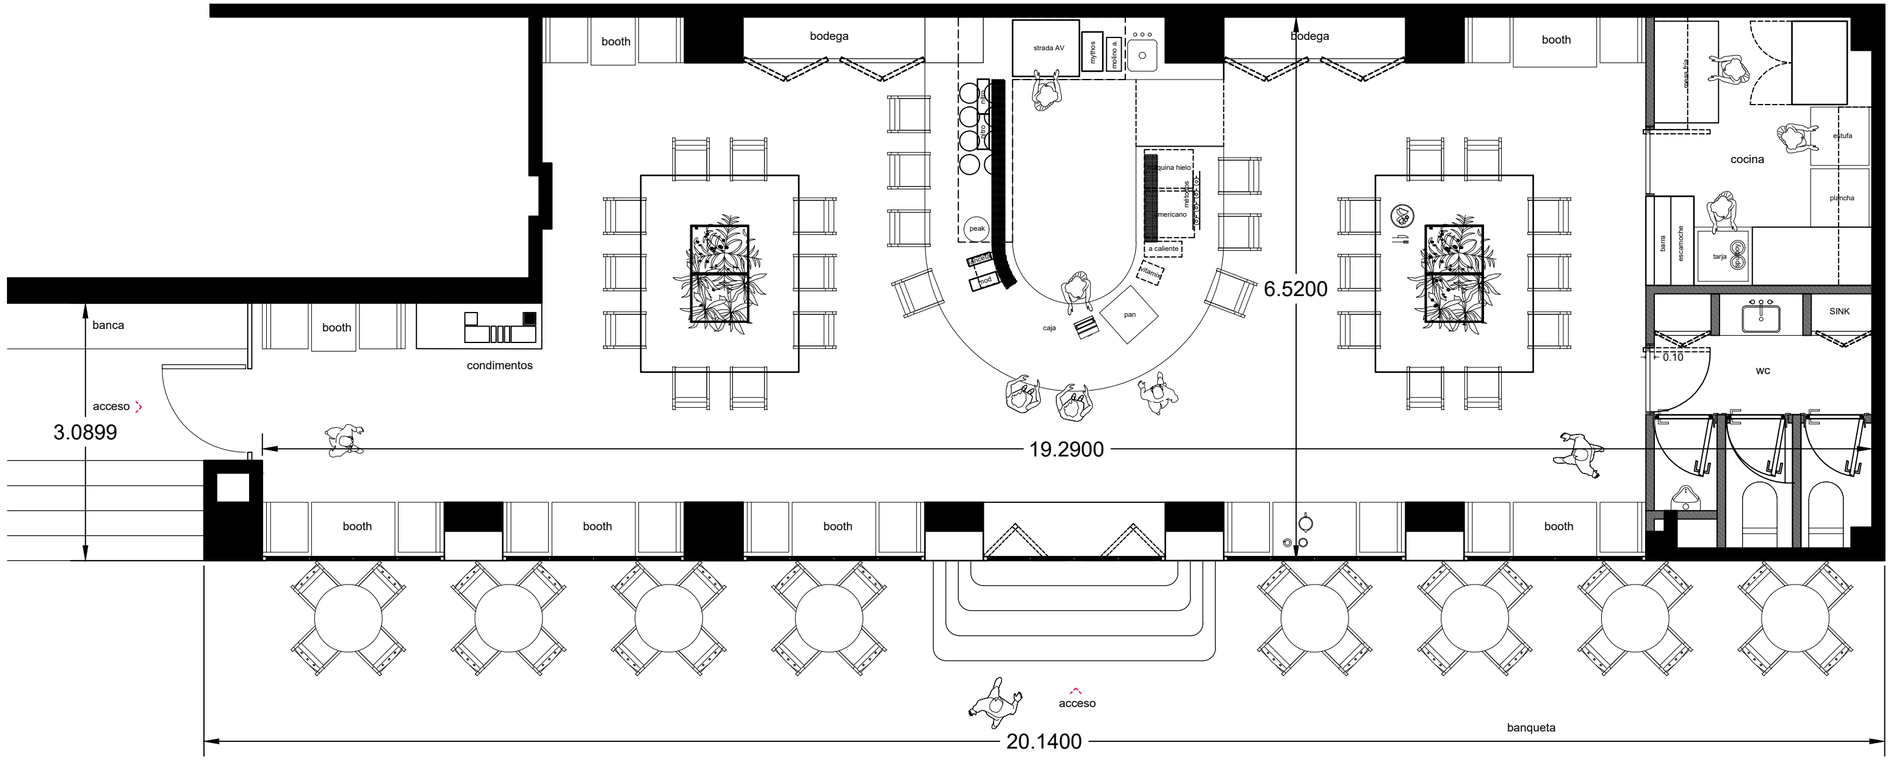
booth
bodega
strada AV
mythos
mobico a
bodega
booth
mesa fría
cocina
estufa
plancha
barra
escamoche
tarja
SINK
0.10
wc
peak
americano
caja
pan
6.5200
banca
booth
condimentos
acceso
3.0899
19.2900
booth
booth
booth
booth
acceso
20.1400
banqueta

DOMĚSTIKA